



CONCEPT, NOT FOR FABRICATION

SlopeWatch · github.com/BoujeeEnjinia1701/slopewatch

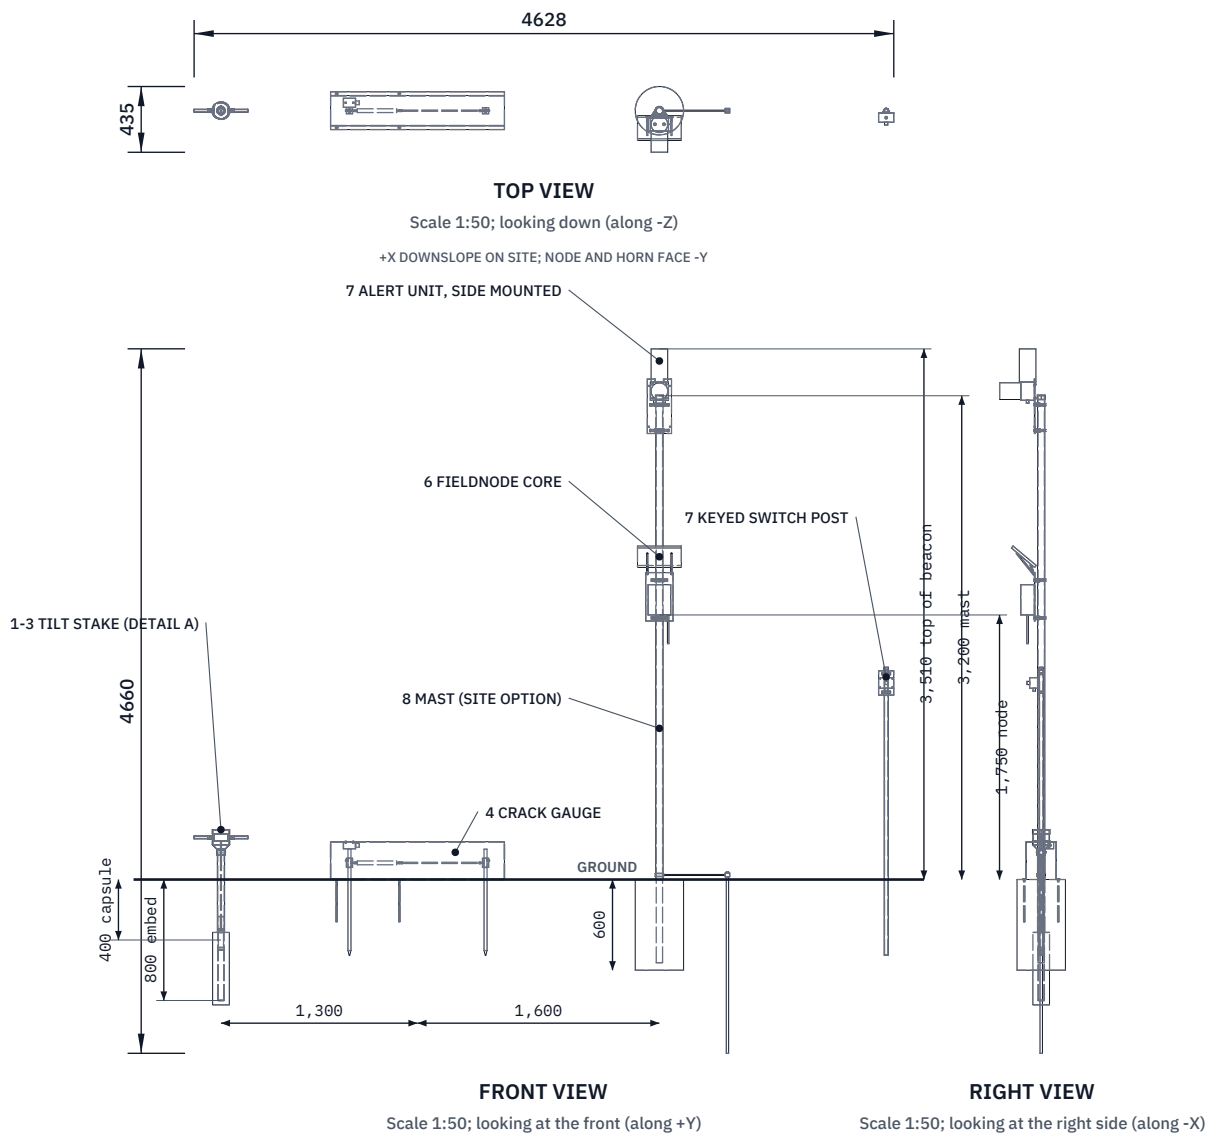

REV	DESCRIPTION	DATE	BY
P1	Preliminary GA for TRL 3 (from cad/src/model.py)	2026-09-25	AC
P2	Keyed switch on own post 5 m from mast; mast a site option (DDR-002)	2026-09-25	AC
P3	Layout and labels tidied	2026-09-25	AC
P4	Constructable design (DDR-003)	2026-10-01	AC
P5	SLW-DEC-001: stake head marking, back plate wall holes	2026-10-02	AC

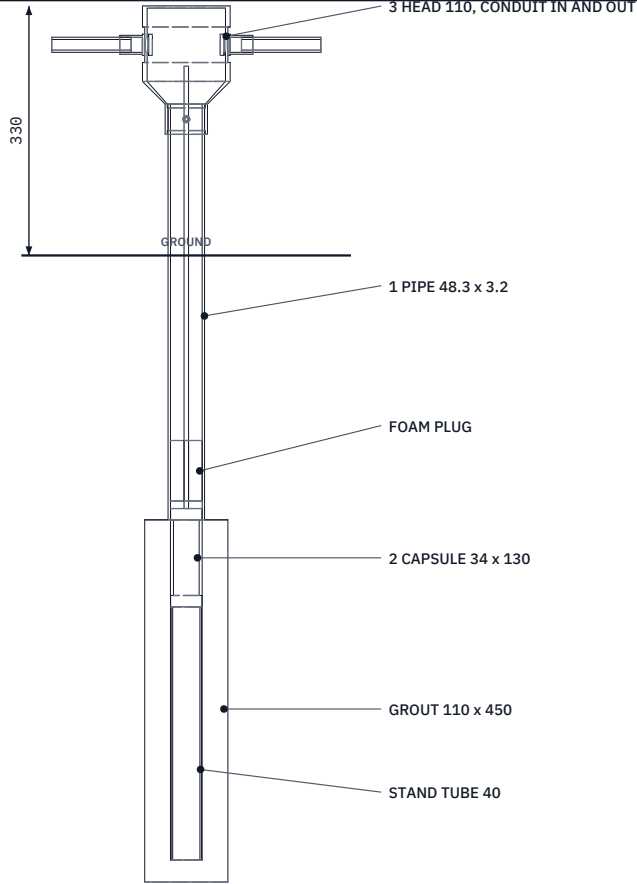

MAIN DIMENSIONS AND INTERFACES (MM)

Stake 48.3 x 3.2 galv. pipe, 1000 long, 800 in ground, screwed end cap

Hole 110 dia x 829; grout 3.7 L; capsule 400 deep on stand tube

Crack gauge: anchors 900 apart, pins 20 x 700, stroke 100

Mast (option) 48.3 x 3.2, 3,200 high; footing 320 x 600

Switch post 26.9 dia, 1,400 high, 5 m from mast on site

FieldNode massing per FND-DDR-003; node bottom 1,750; alert unit on V-blocks and bands

Bus 4-core 0.5 mm2 on the 5 V port; stakes 10 m apart, cable 59 m on site

SLOPEWATCH

github.com/BoujeeEnjinia1701/slopewatch

General arrangement

DRAWING NO. SLW-DWG-001			REV P5	SHEET 1 of 1	SIZE ANSI B
SCALE 1:50	UNITS mm	PROJECTION 	DATE 2026-10-02	DRAWN Amish Chadha	

MATERIAL / NOTES
Galvanized steel, cement grout, bought-in parts per bom/bom.csv. PRELIMINARY, NOT FOR FABRICATION