



CONCEPT, NOT FOR FABRICATION

SlopeWatch · github.com/BoujeeEnjinia1701/slopewatch

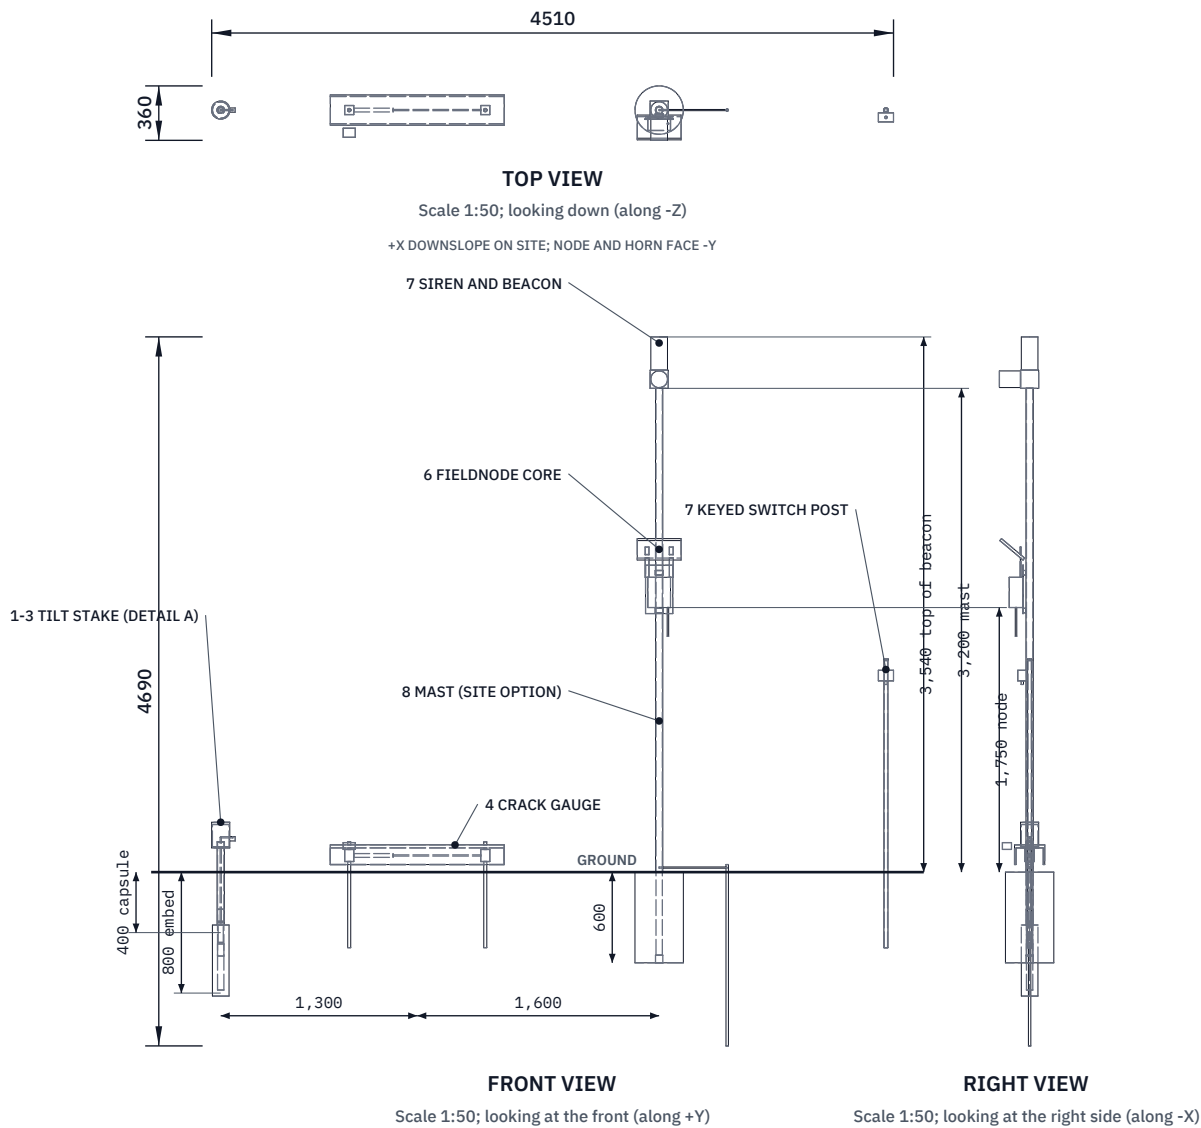

REV	DESCRIPTION	DATE	BY
P1	Preliminary GA for TRL 3 (from cad/src/model.py)	2026-09-25	AC
P2	Keyed switch on own post 5 m from mast; mast a site option (DDR-002)	2026-09-25	AC
P3	Layout and labels tidied	2026-09-25	AC

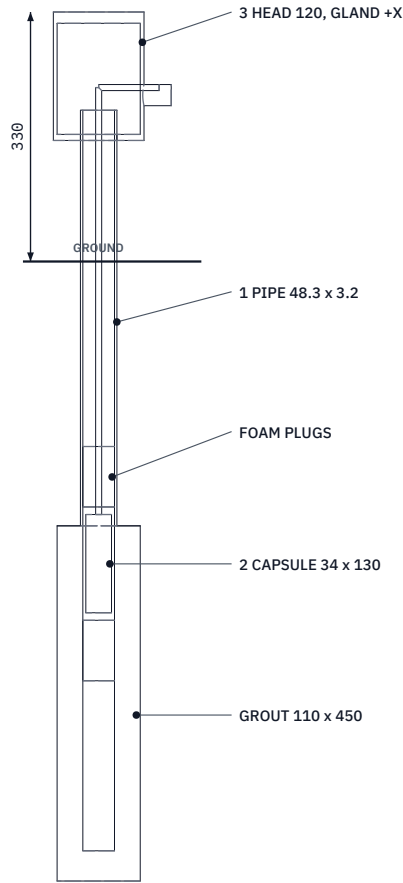

MAIN DIMENSIONS AND INTERFACES (MM)

- Stake 48.3 x 3.2 galv. pipe, 1000 long, 800 in ground
- Grout 110 dia x 450, 3.6 L; capsule 400 deep
- Crack gauge: anchors 900 apart, pins 20 x 700, stroke 100
- Mast (option) 48.3 x 3.2, 3,200 high; footing 320 x 600
- Switch post 26.9 dia, 1,400 high, 5 m from mast on site
- FieldNode massing per FND model; node bottom 1,750
- Bus: 4-core 0.5 mm² on the 5 V port; alert unit on the 12 V port
- Site: stakes 10 m apart on the fall line; cable 59 m (sheet spacing is not site spacing)

SLOPEWATCH

github.com/BoujeeEnjinia1701/slopewatch

General arrangement

DRAWING NO. SLW-DWG-001			REV P3	SHEET 1 of 1	SIZE ANSI B
SCALE 1:50	UNITS mm	PROJECTION 	DATE 2026-09-25		DRAWN Amish Chadha
MATERIAL / NOTES Galvanized steel, cement grout, bought-in parts per bom/bom.csv. PRELIMINARY, NOT FOR FABRICATION					
Licensed CERN-OHL-S-2.0 · Design Molecule Lab · designmolecule.com			Generated from cad/src; do not edit by hand		