



CONCEPT, NOT FOR FABRICATION


REV	DESCRIPTION	DATE	BY
P1	Concept sheet	2026-09-25	AC

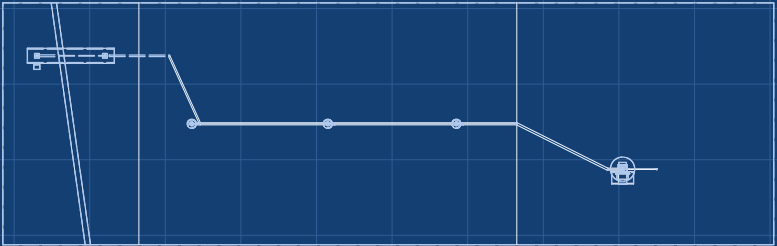


TOP VIEW
Scale 1:100

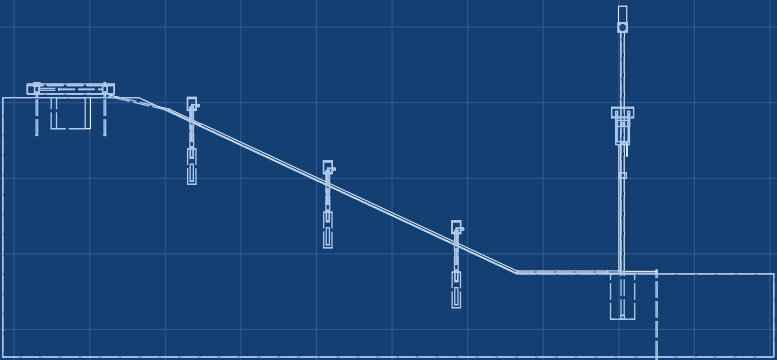

FRONT VIEW
Scale 1:100

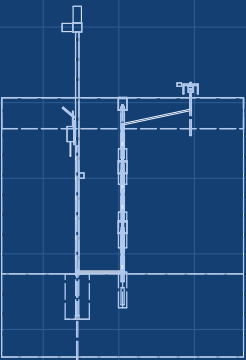

RIGHT VIEW
Scale 1:100

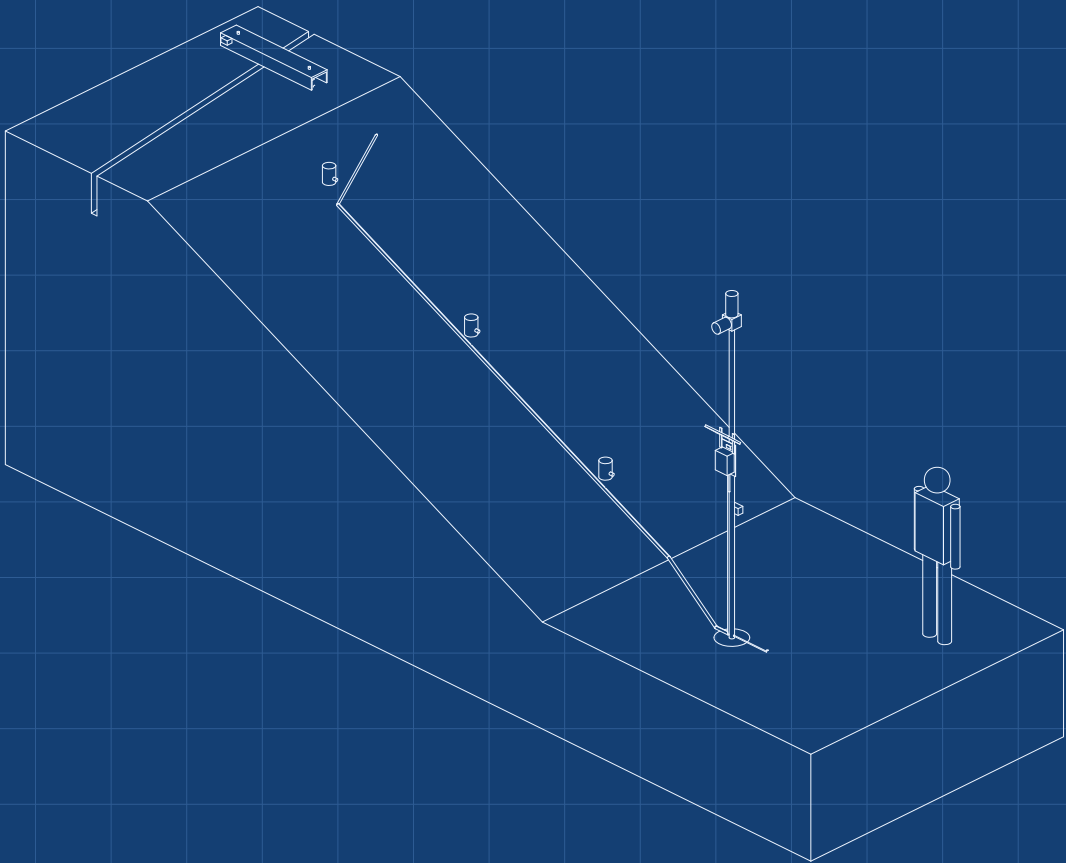

ISOMETRIC VIEW
Not to scale; grey is for scale

KEY FIGURES

3 grouted tilt stakes, capsule 0.4 m deep; 0.0055 deg output step
Precaution 0.01 deg/h, warning 0.1 deg/h (adopted for TRL 3, open for review)
Thermal drift 0.0012 deg/h worst case (wet soil), R2 limit 0.002
Reads every 10 min; siren 13 s after a confirmed warning
\$261 SlopeWatch parts (\$237 on an existing pole); FieldNode \$126 extra

SLOPEWATCH

Slope movement monitor concept

DRAWING NO.

SLW-DWG-010

REV

P1

SHEET

1 of 1

SIZE

ANSI B

SCALE

1:100

UNITS

mm

PROJECTION



DATE

2026-09-25

DRAWN

Amish Chadha

MATERIAL / NOTES

Massing model for concept communication